

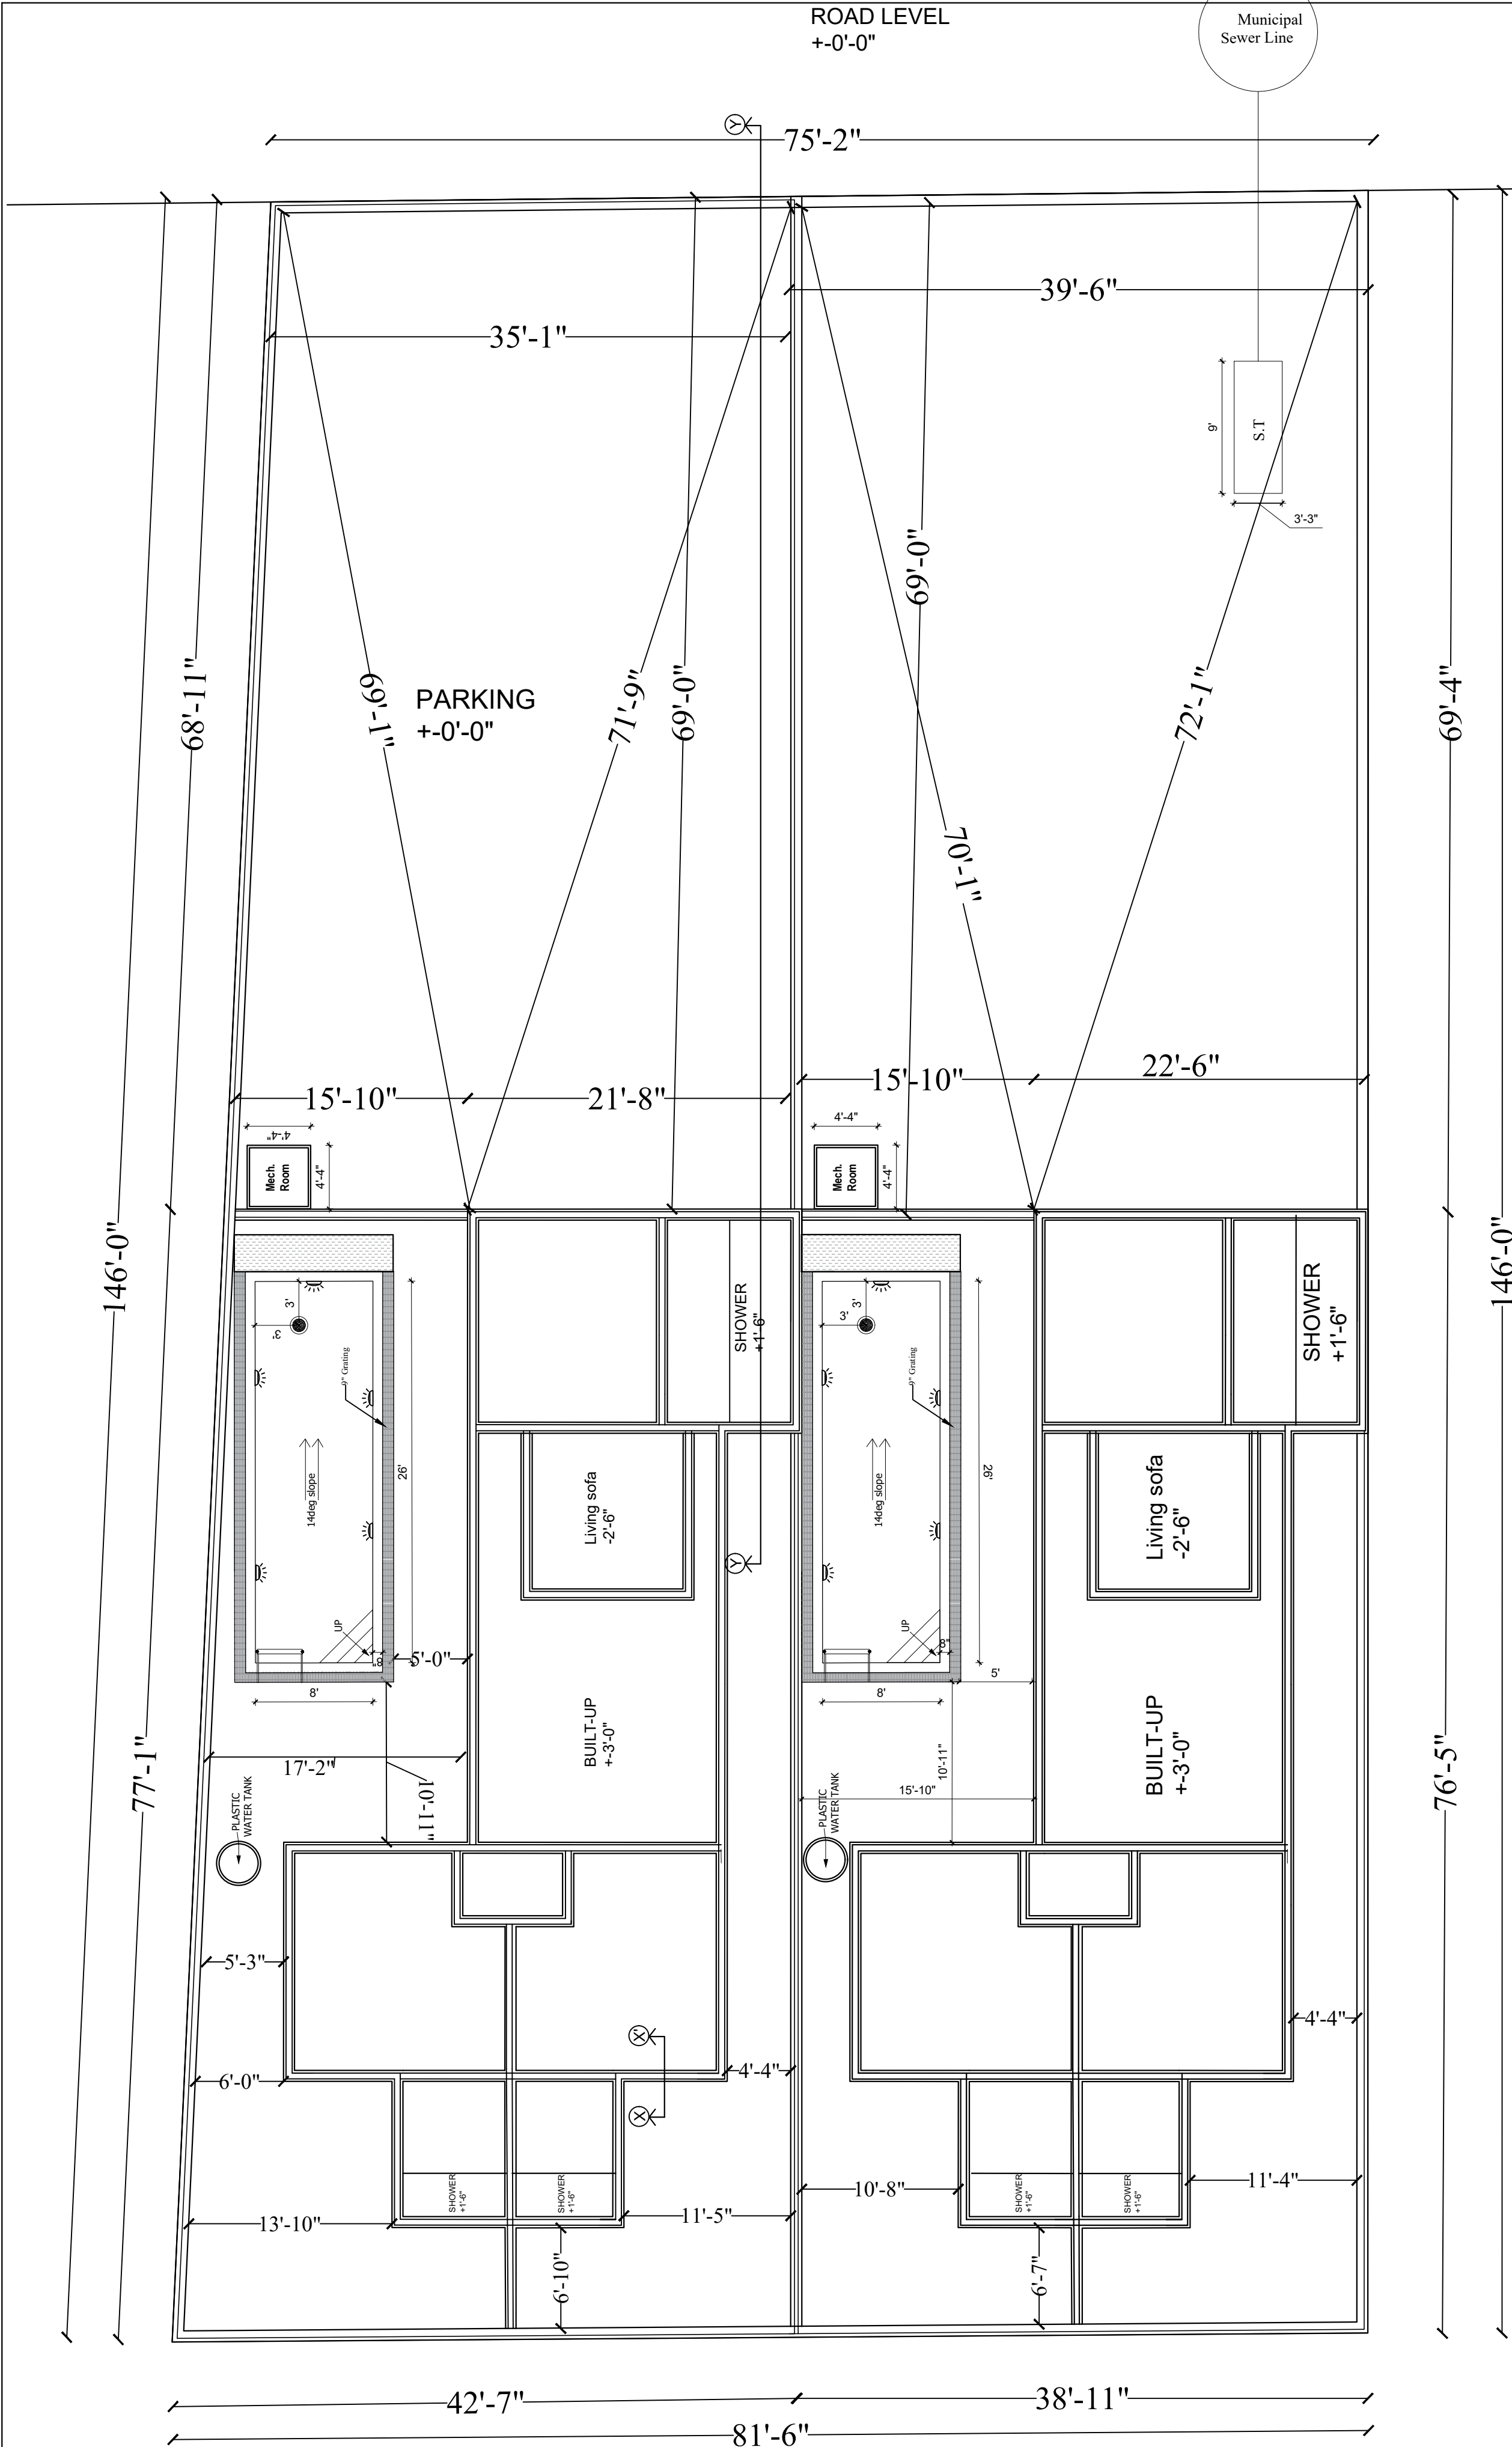
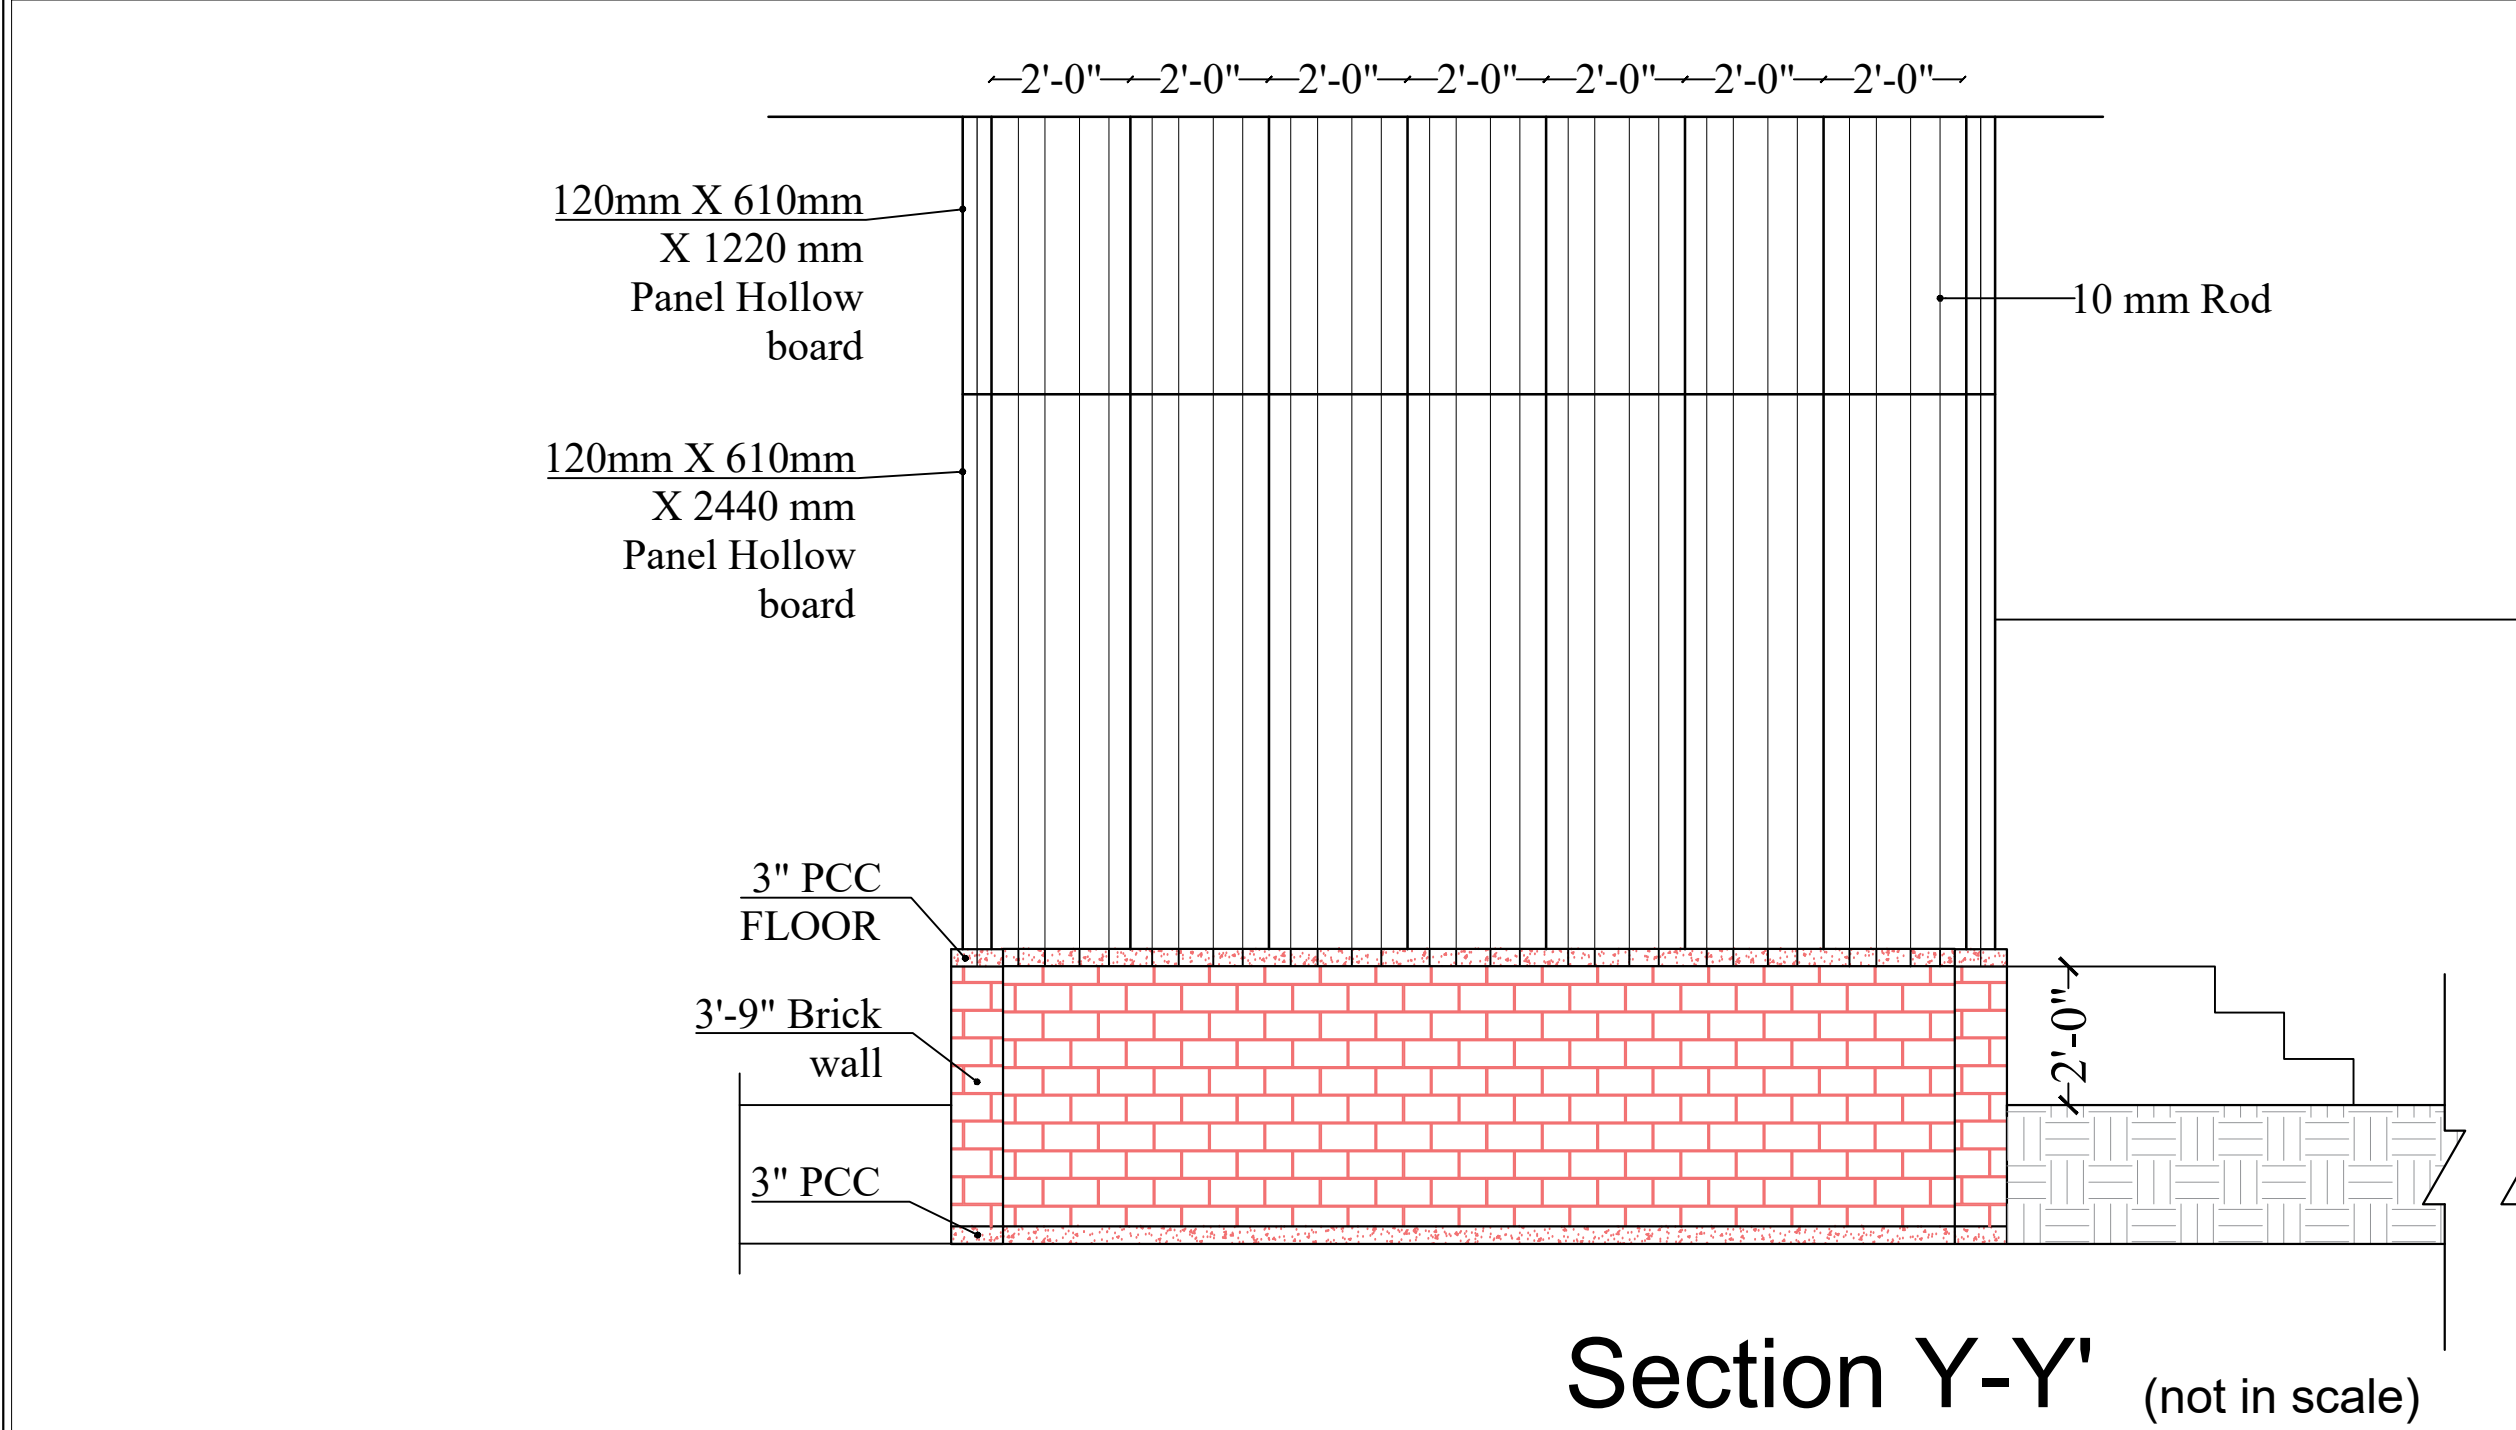


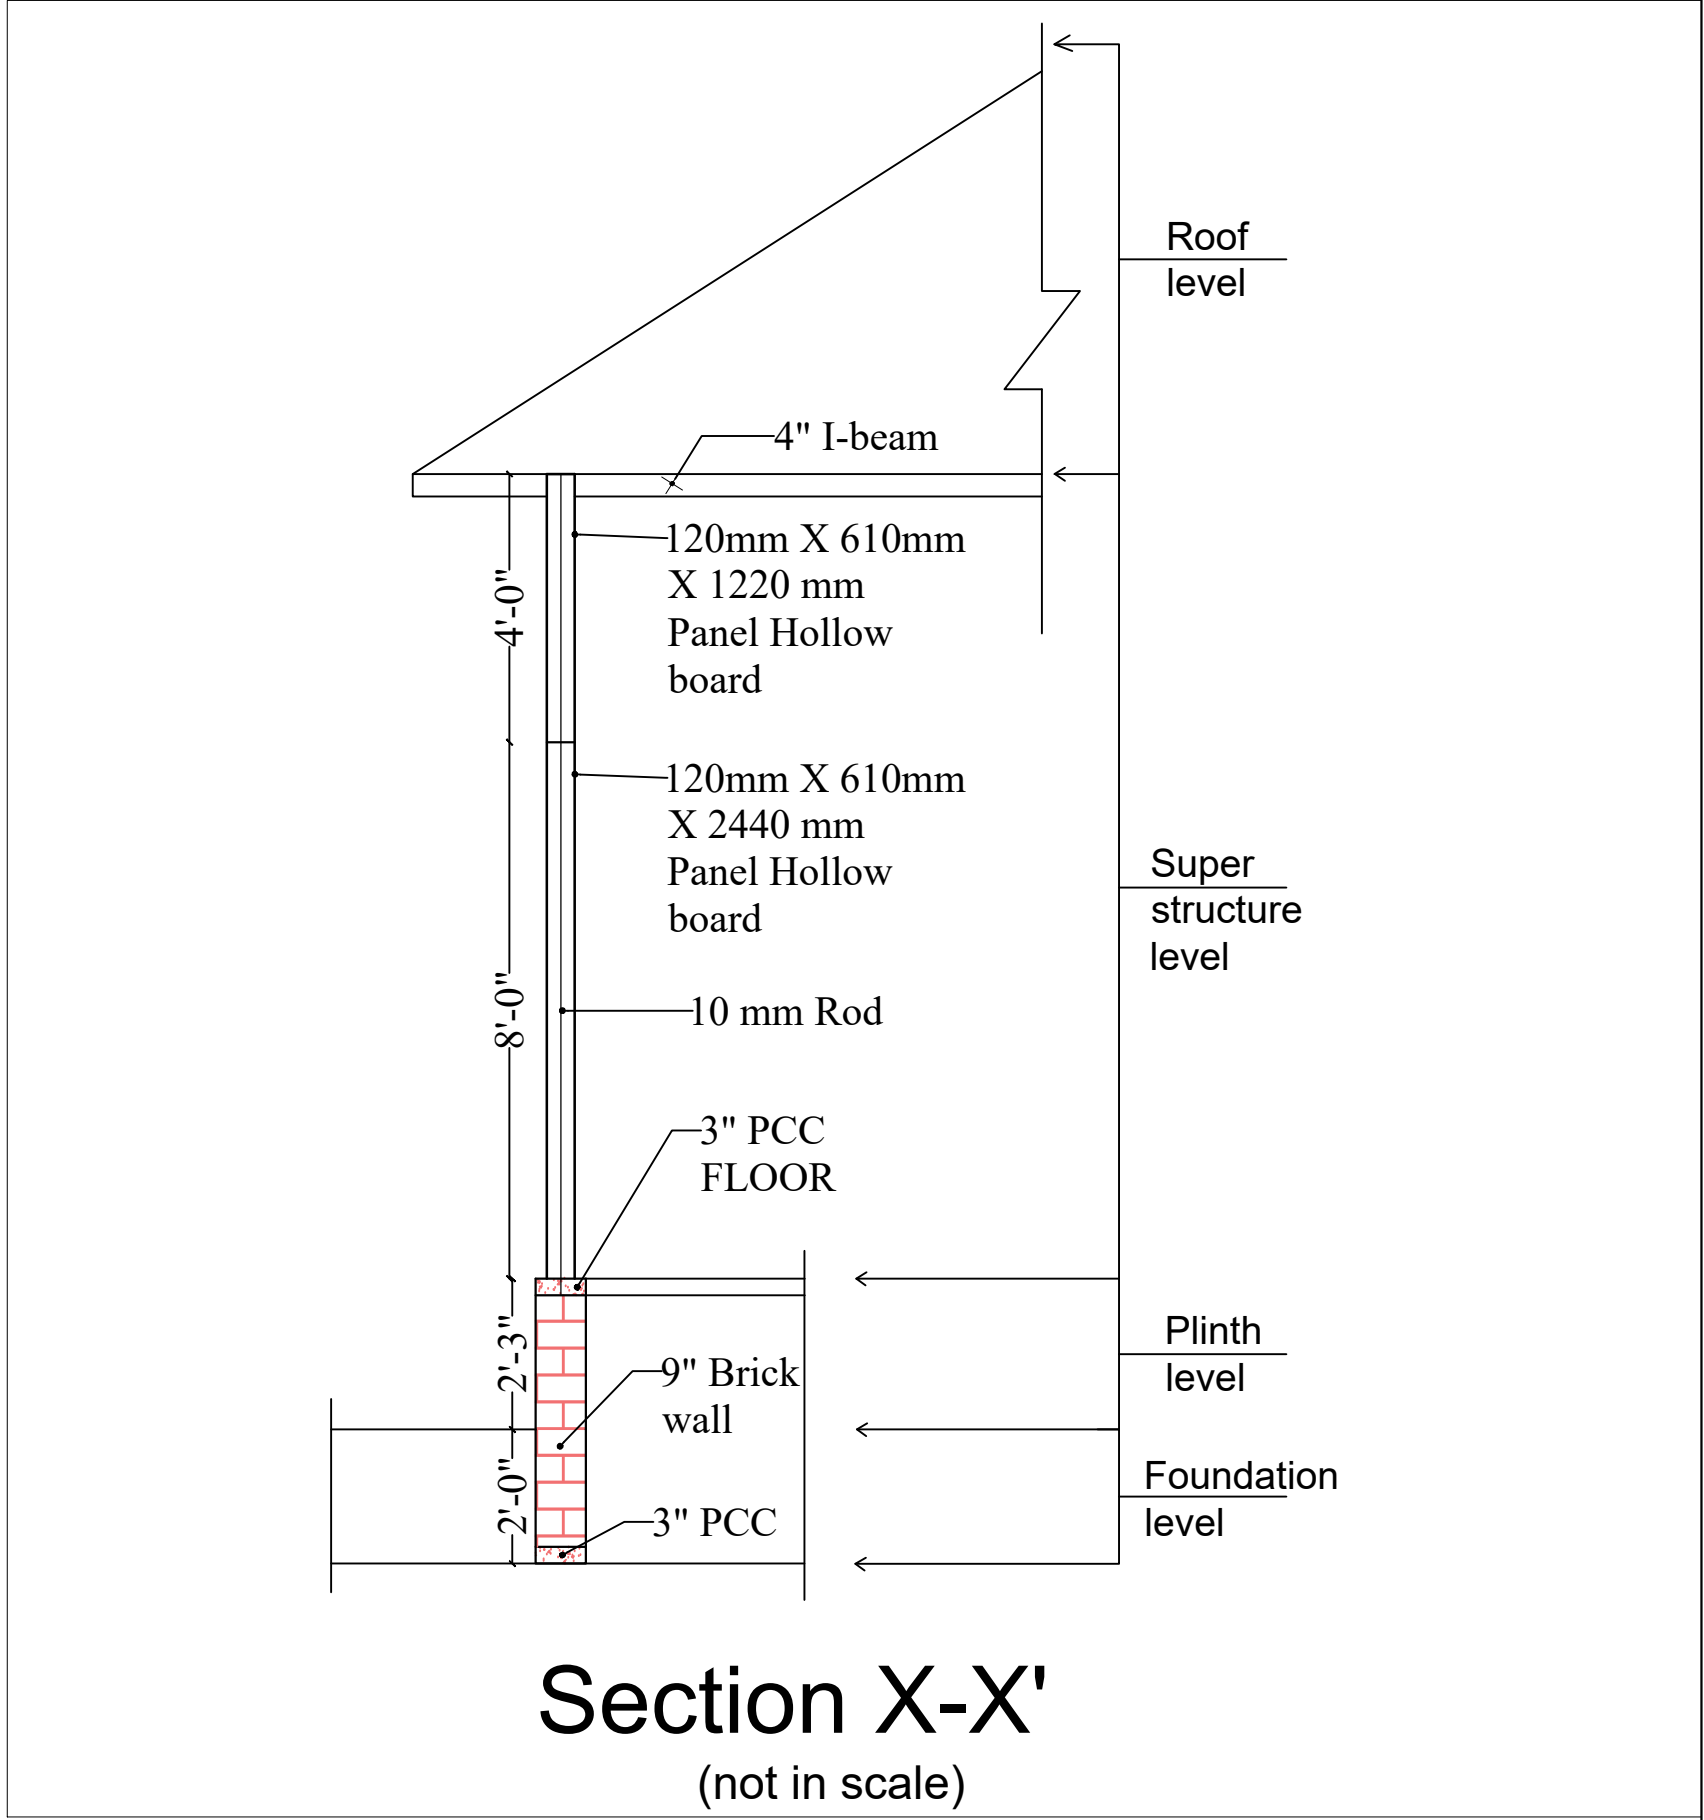

9' wide TRENCH PLAN

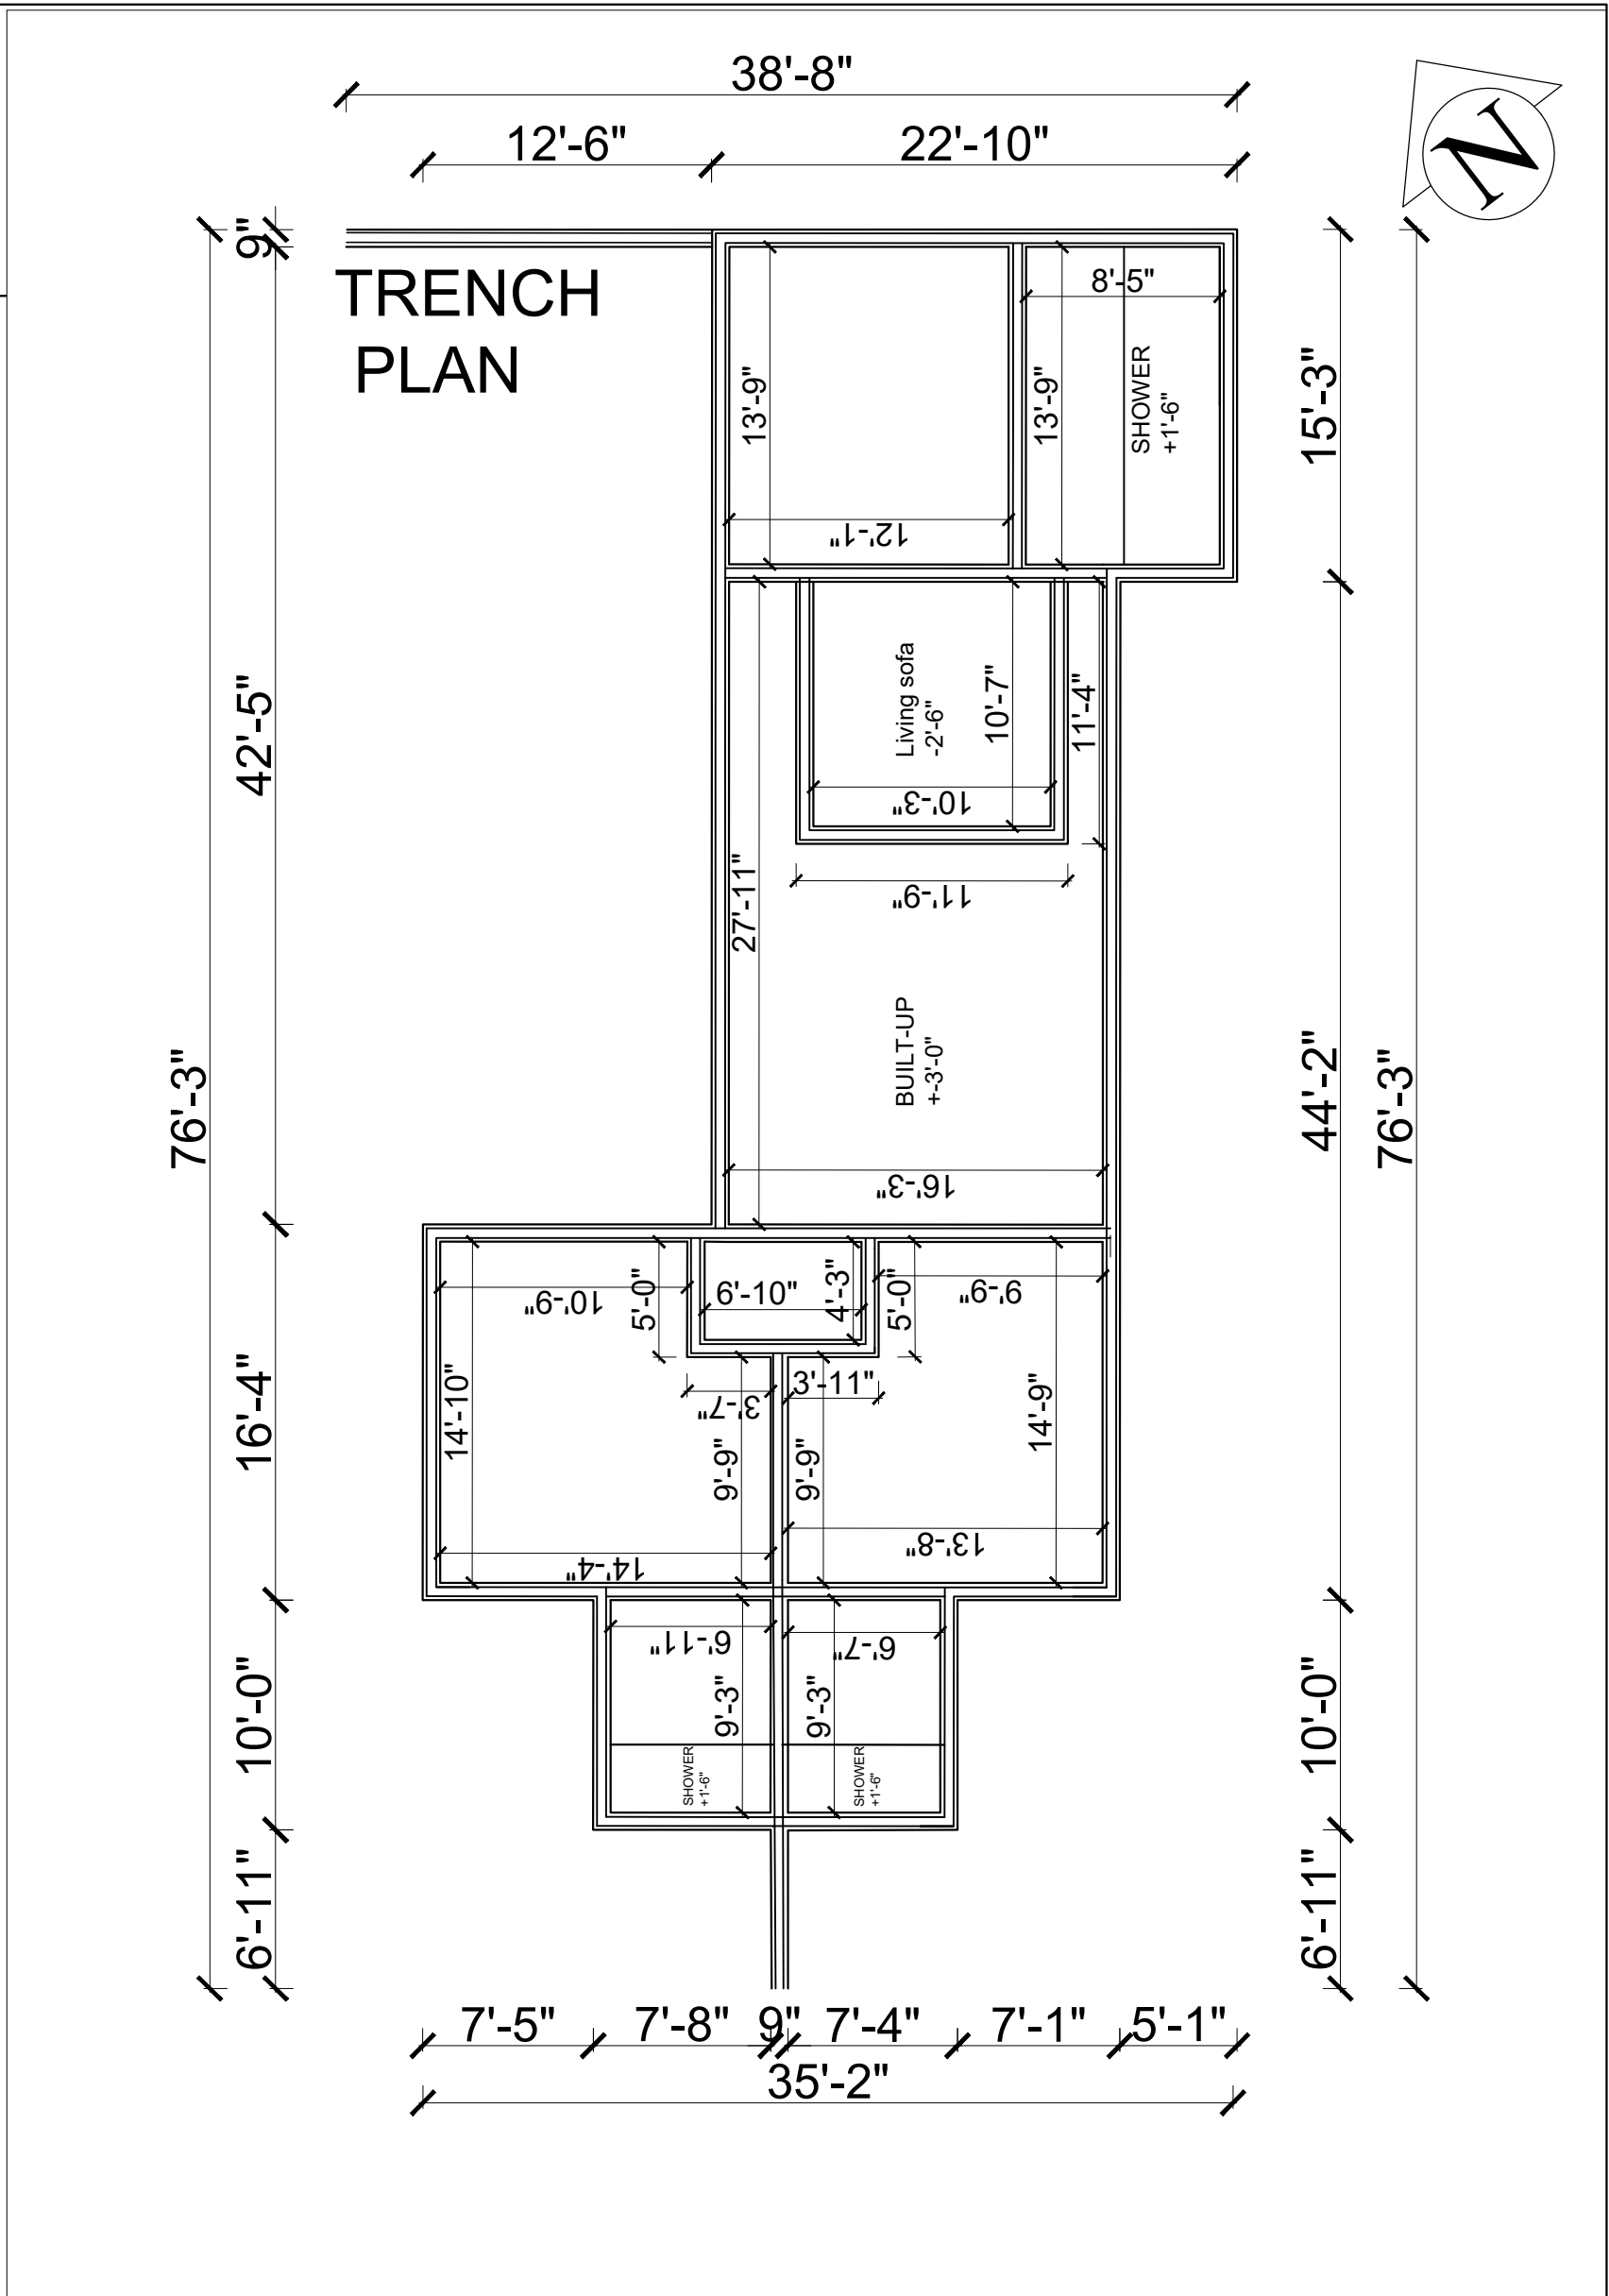

Section Y-Y' (not in scale)

FOR OFFICIAL USE ONLY	OWNER:	TITLE : TRENCH PLAN & DETAIL		SIDE PLOTS (SADHIYAR) DETAILS:			DRAWN BY: ANUSHKA KHATRI		DESIGNED BY: ANUSHKA KHATRI												
		BUILDING TYPE: VILLA	LOCATION: CHITWAN				CHECKED BY:														
	SIGNATURE:	PLOT NO: 1224	LAND AREA PER CADESTRAL MAP: 1059 SQ.M LAND AREA AS PER FIELD:	<table><tr><td>S.N</td><td>DIRECTION</td><td>PLOT NUMBER & NAME</td></tr><tr><td>1</td><td>EAST</td><td>1234</td></tr><tr><td>2</td><td>WEST</td><td>1398</td></tr><tr><td>3</td><td>NORTH</td><td>1223 Road</td></tr><tr><td>4</td><td>SOUTH</td><td>327</td></tr></table>	S.N	DIRECTION					PLOT NUMBER & NAME	1	EAST	1234	2	WEST	1398	3	NORTH	1223 Road	4
		S.N	DIRECTION	PLOT NUMBER & NAME																	
1	EAST	1234																			
2	WEST	1398																			
3	NORTH	1223 Road																			
4	SOUTH	327																			